



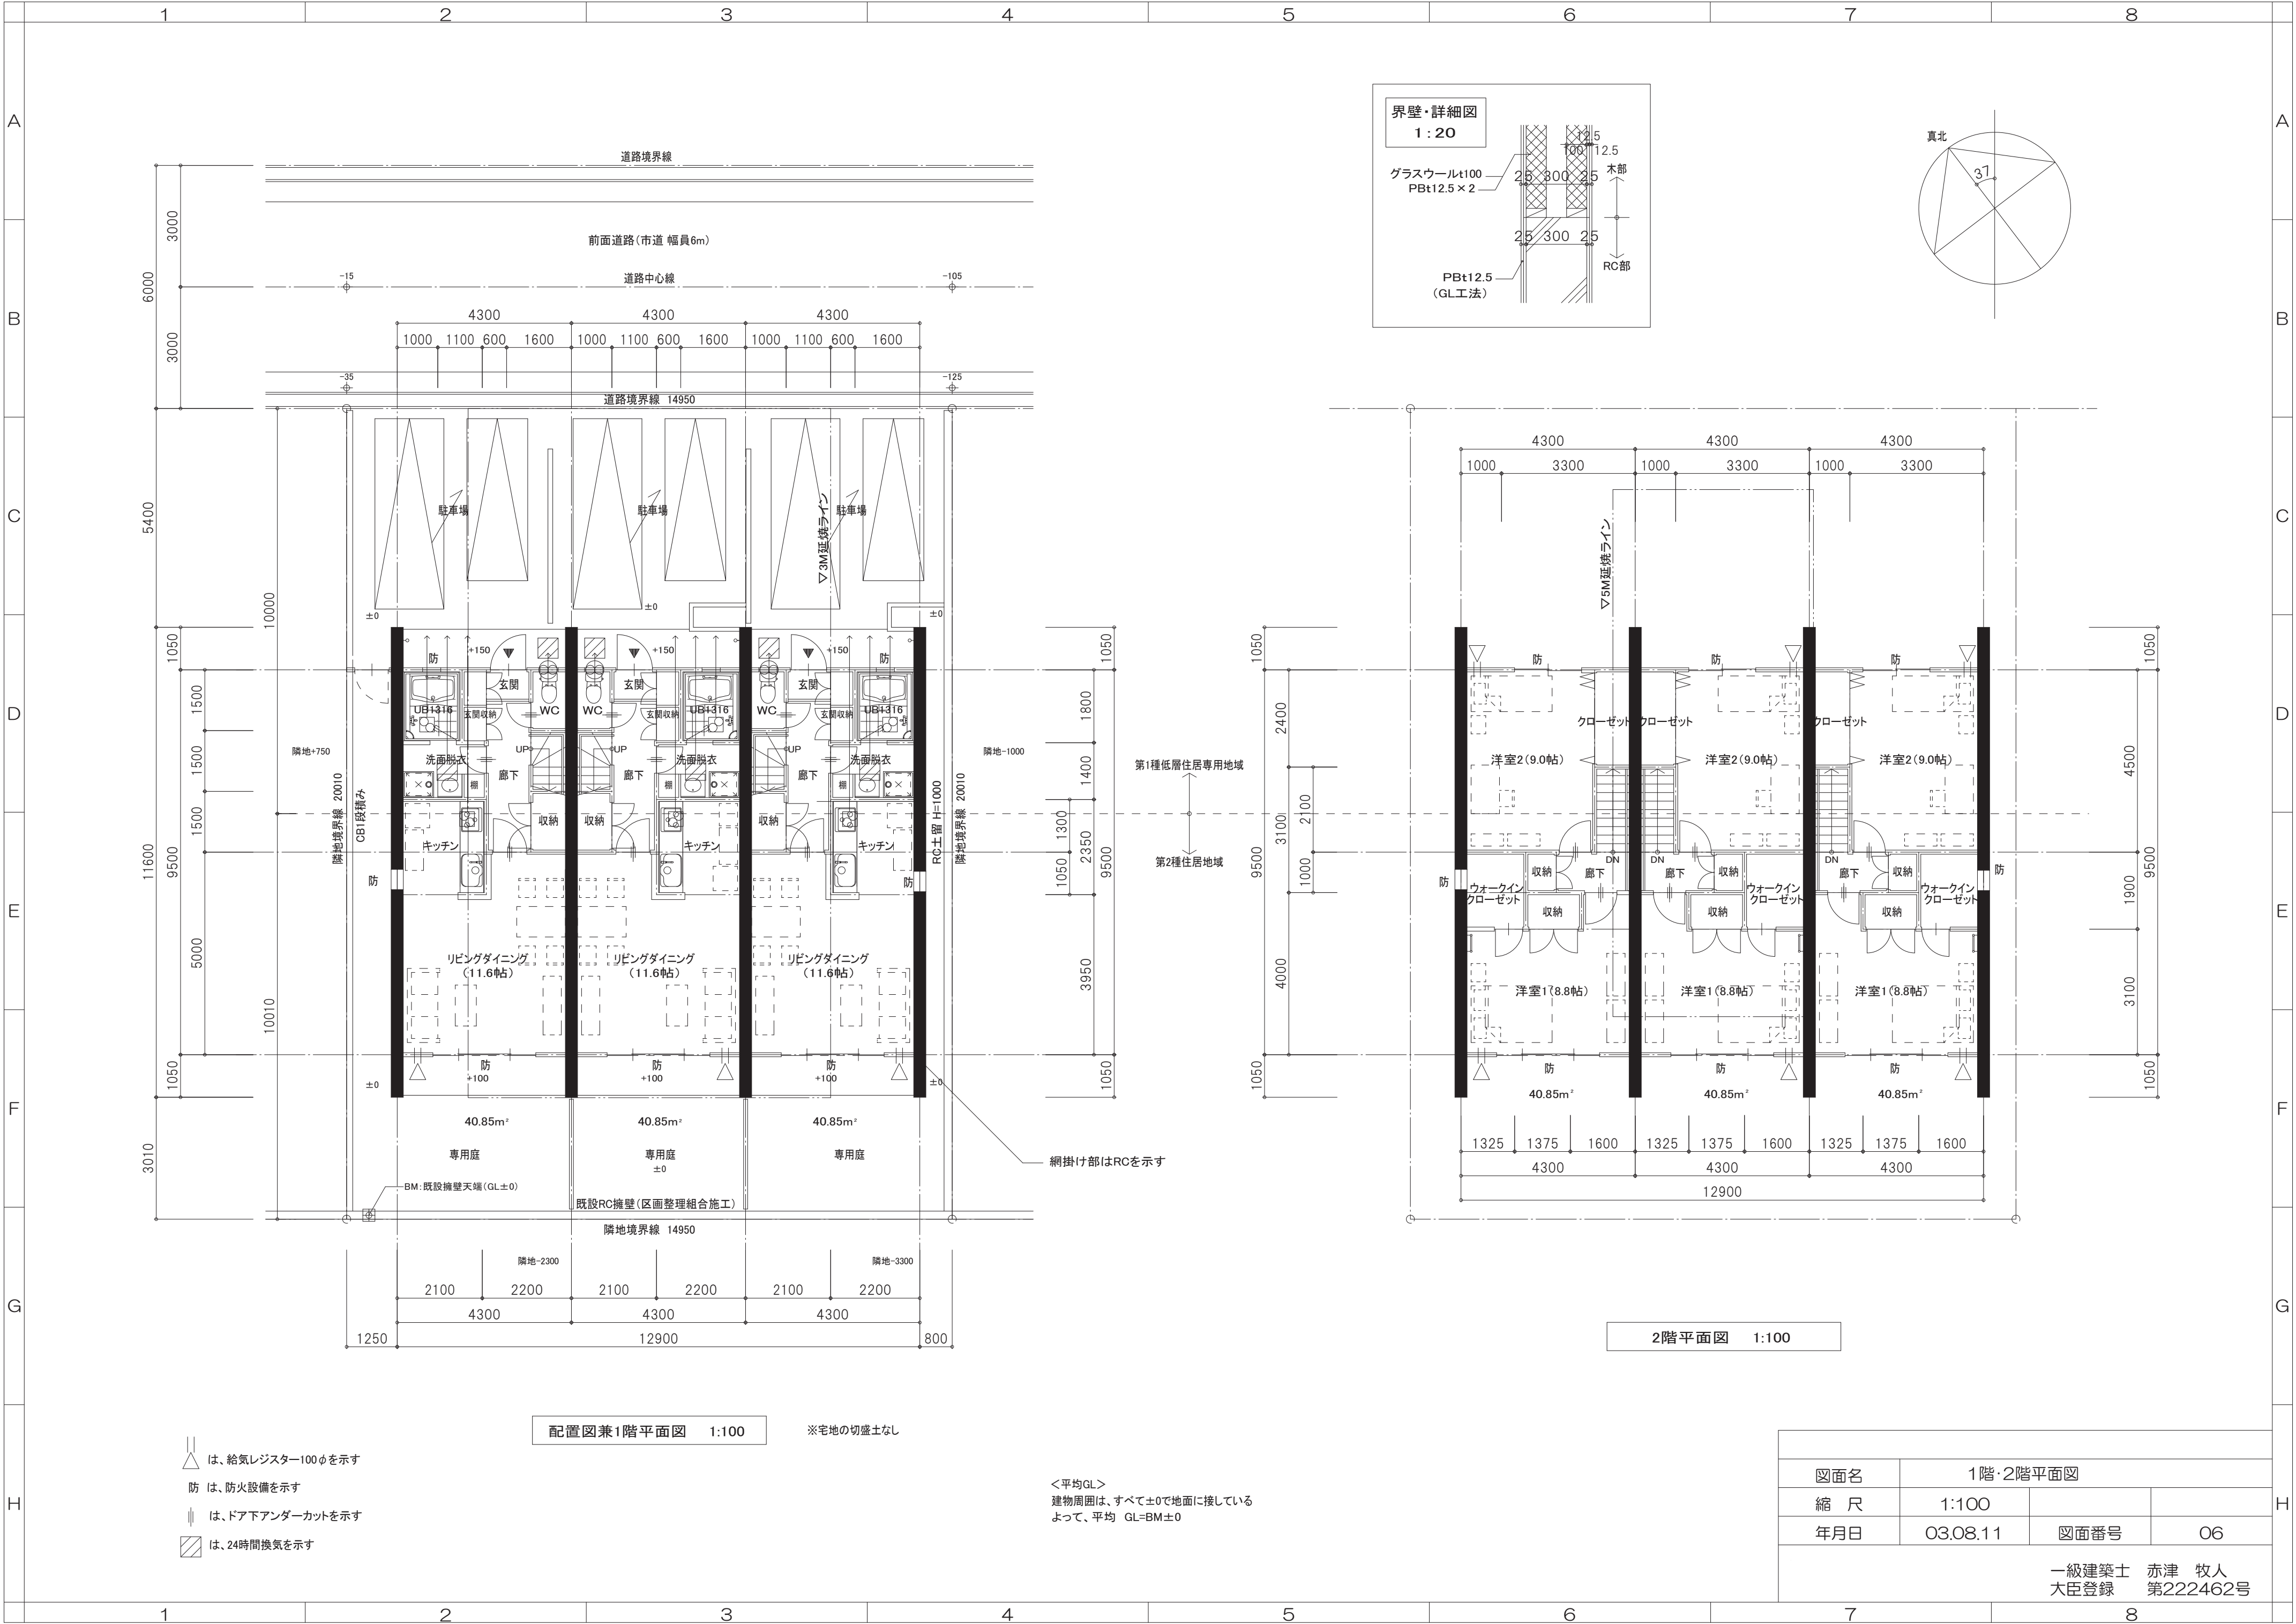

図面名			
1階・2階平面図			
縮 尺	1:100		
年月日	03.08.11	図面番号	06
一級建築士 赤津 牧人 第222462号			

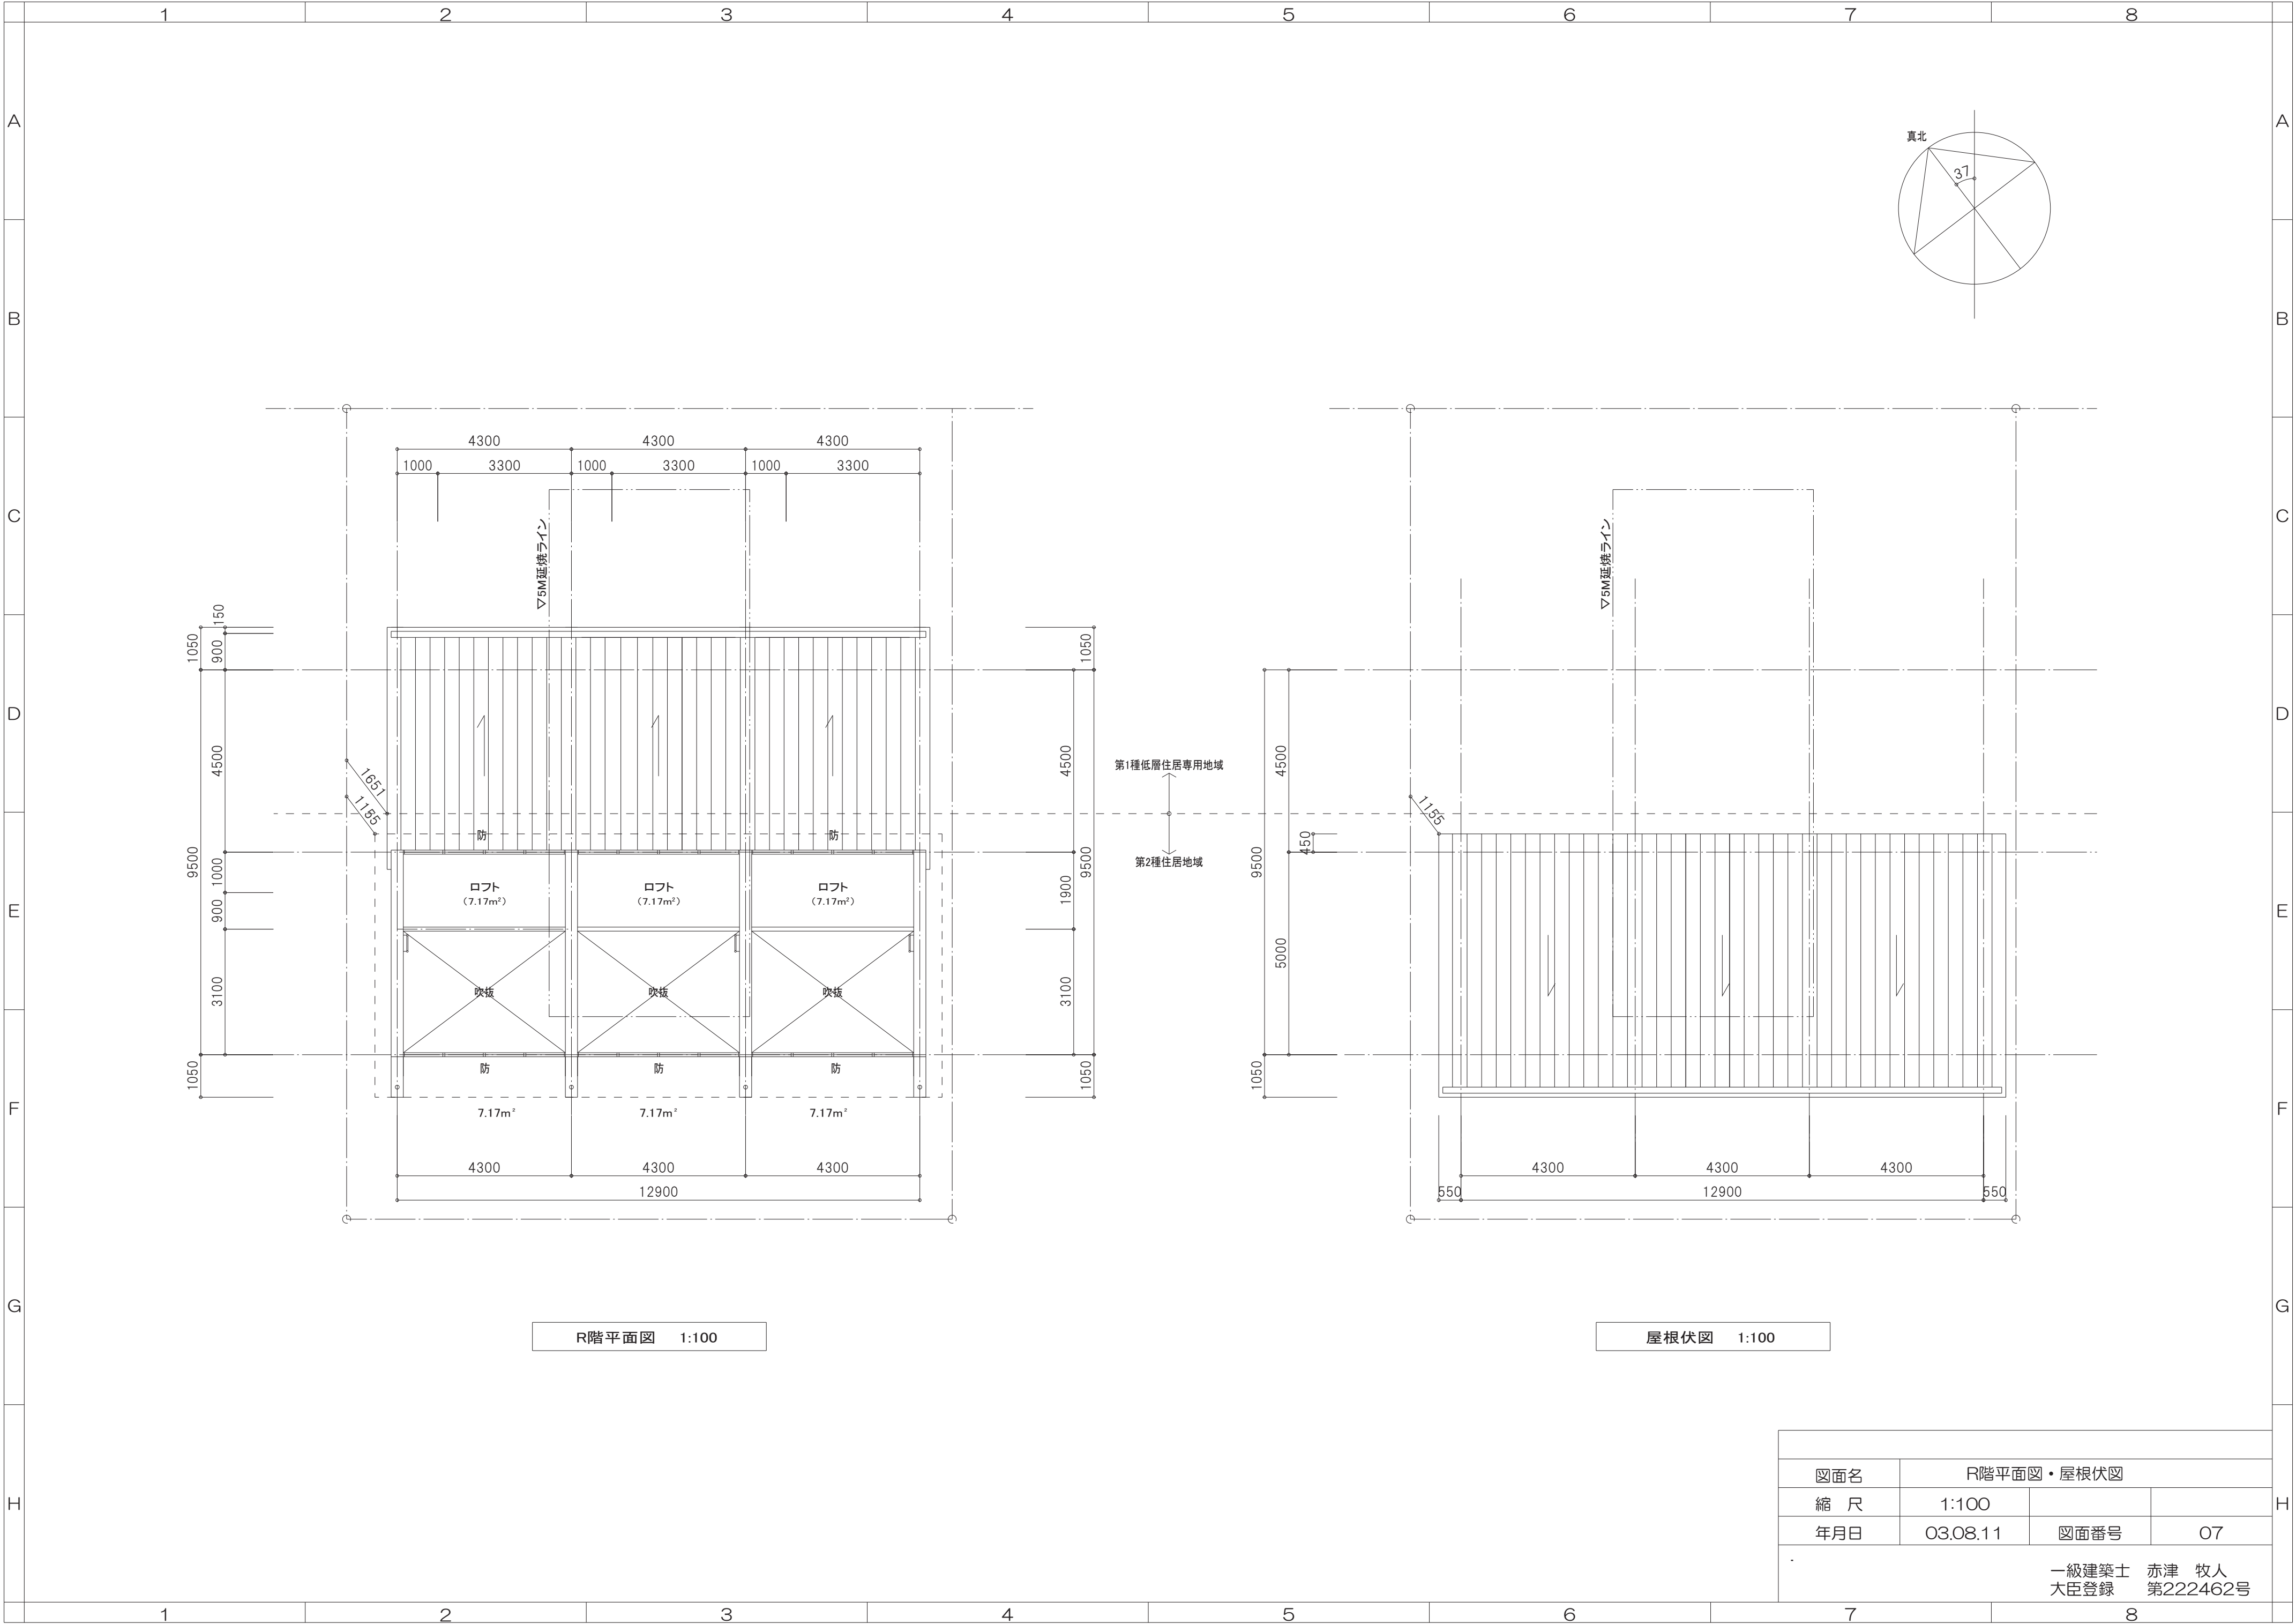


R階平面図 1:100

屋根伏図 1:100

図面名				R階平面図・屋根伏図	
縮 尺		1:100			
年月日		03.08.11		図面番号	
				07	
				一級建築士 赤津 牧人 大臣登録 第222462号	



立面図			
図面名	立面図		
縮 尺	1:100		
年月日	03.08.11	図面番号	08
一級建築士 赤津 牧人 第222462号			

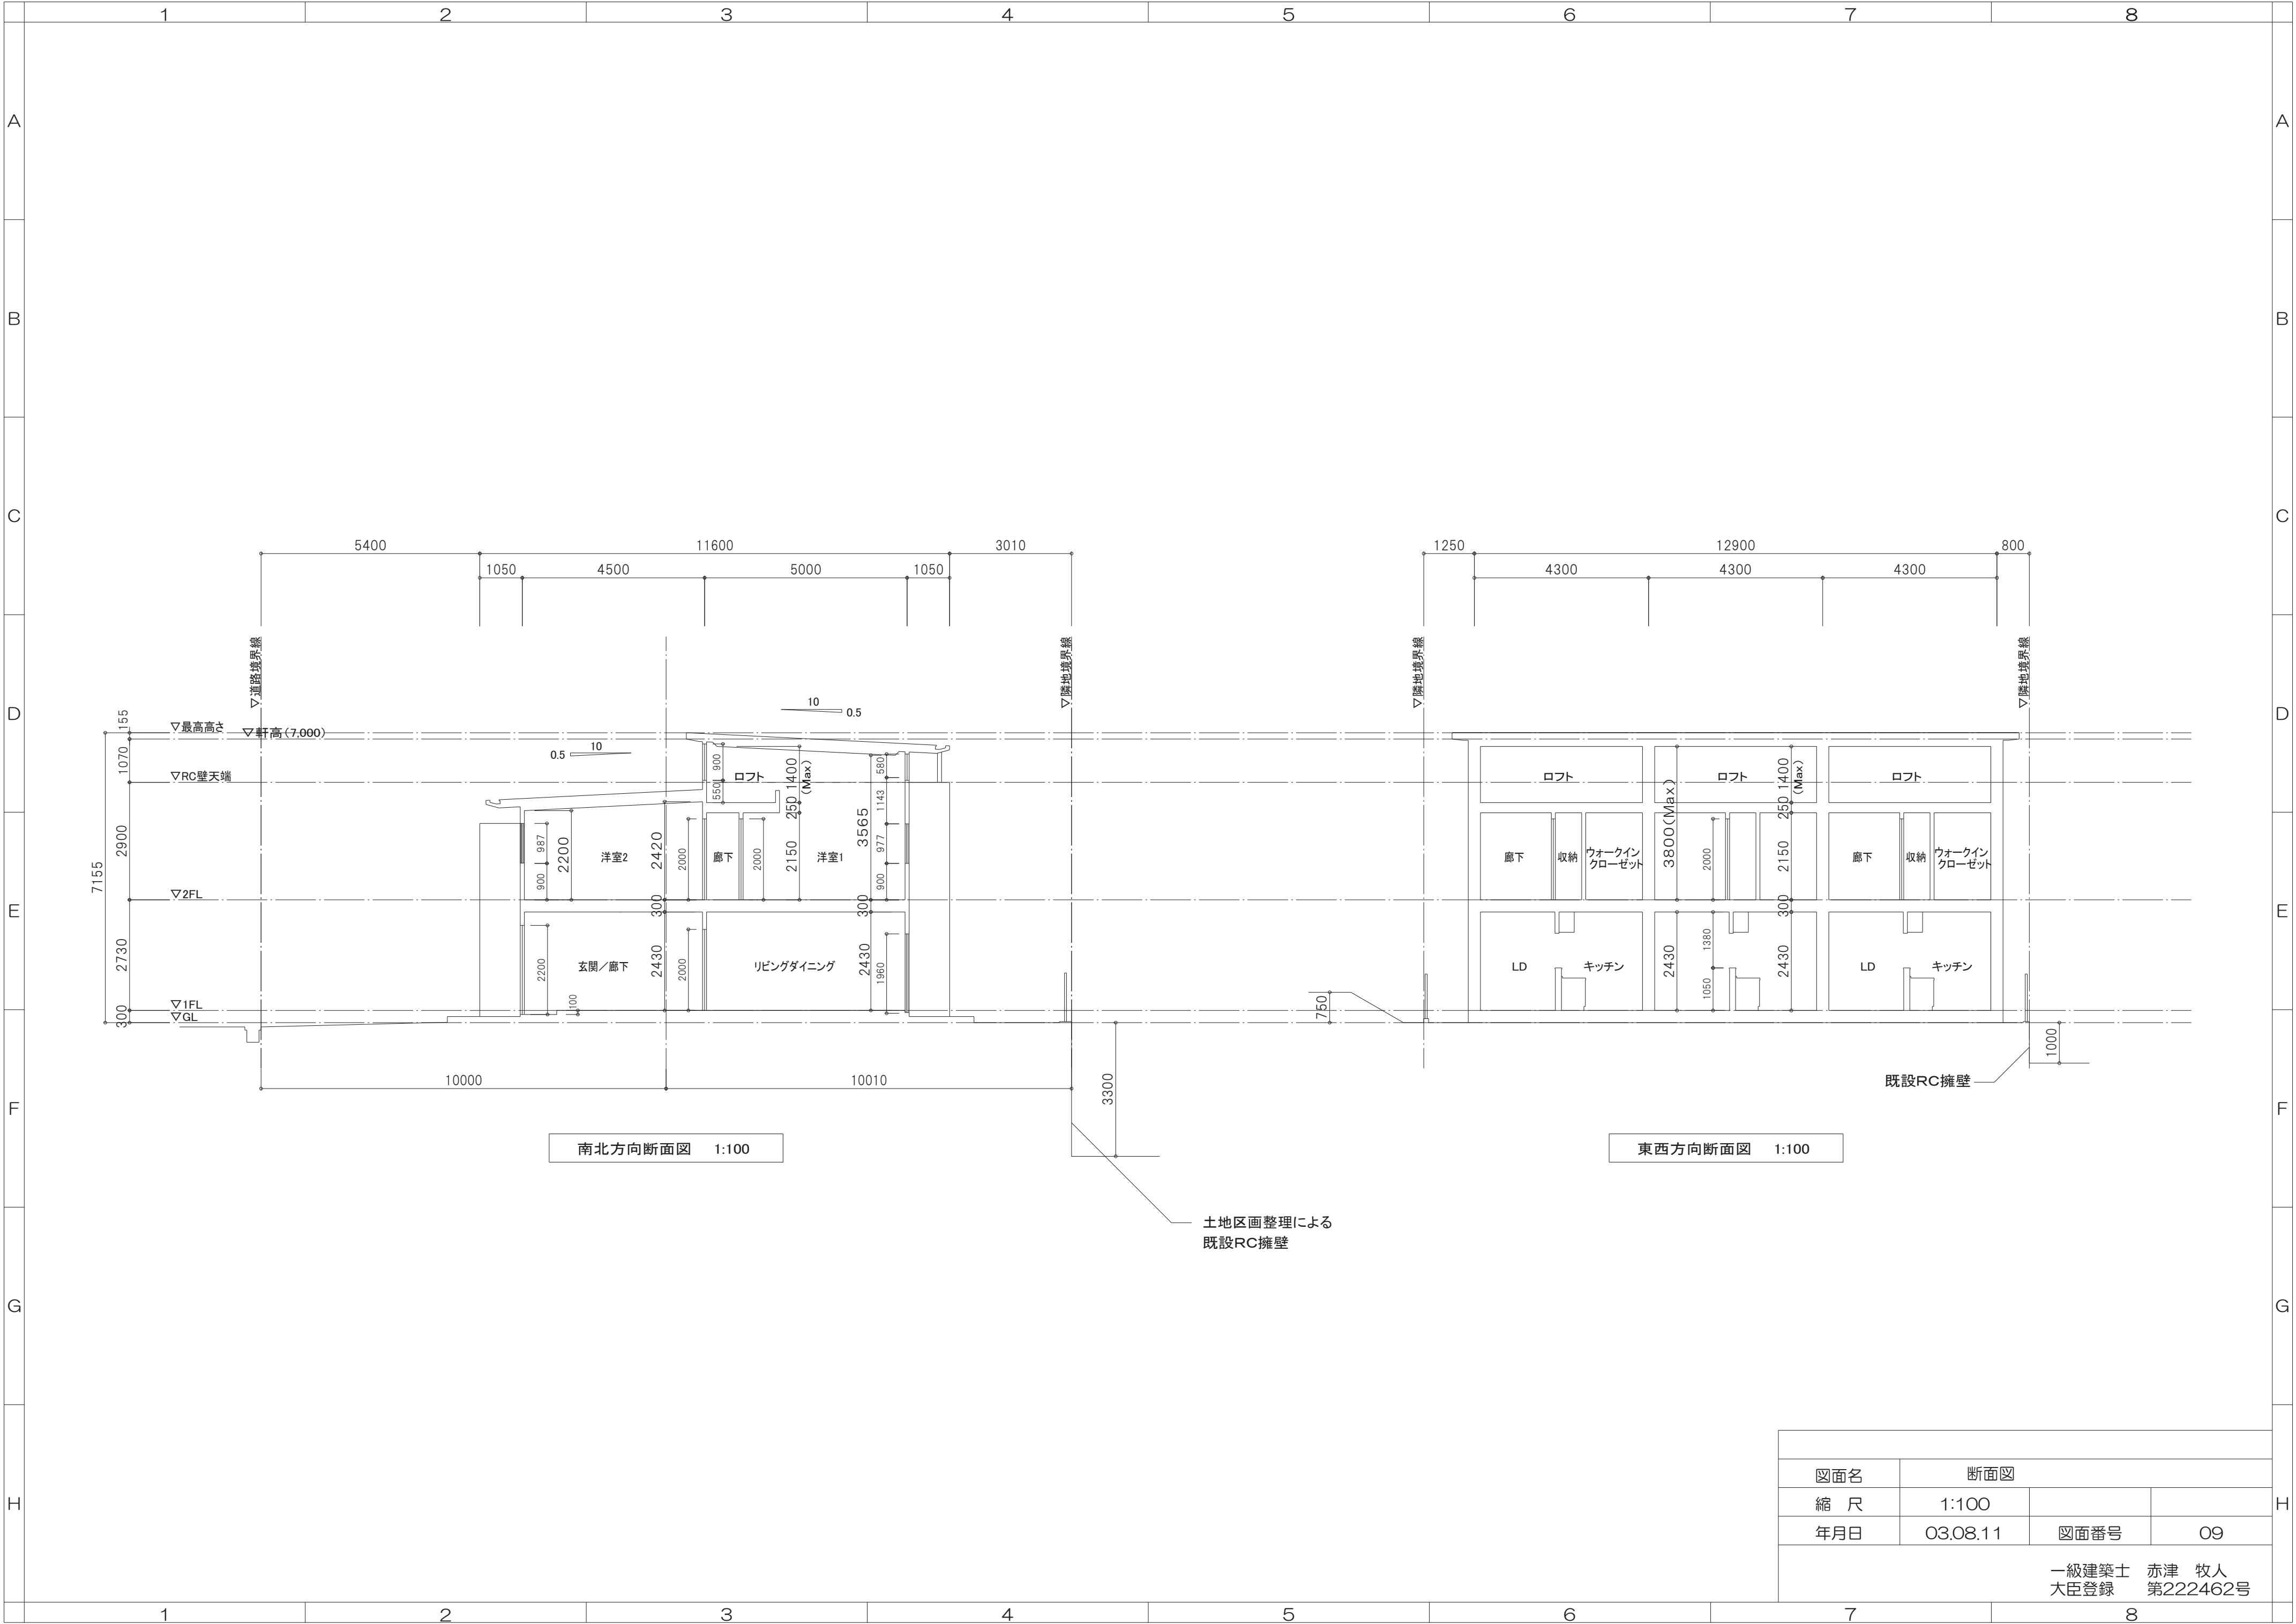

図面名		断面図	
縮 尺	1:100		
年月日	03.08.11	図面番号	09
一級建築士 赤津 牧人 大臣登録 第222462号			

1

2

3

4

5

6

7

8

建築概要

物件名	(仮称)高島共同住宅新築工事	用途地域	第1種低層住居専用地域・第2種住居地域		
所在地	名古屋市天白区高島2丁目710	防火地域	指定無し		
敷地面積	299.21 ㎡(90.52坪)	その他の地域・地区	10m高度地区・20m高度地区		
構造・規模	鉄筋コンクリート造+木造(混構造) 2階建て		宅地造成等規制区域		
建築面積	123.20 ㎡(37.27坪)	建蔽率 41.18%	名古屋市島田東部土地区画事業地内		
延床面積	245.10 ㎡(74.14坪)	容積率 81.92%			
	1階:122.55㎡ 2階:122.55㎡	前面道路	北:6m		
		建ぺい率	50%・60%		
施工床面積	296.7 ㎡(89.75坪)	容積率	150%・200%		

外部仕上表

屋根	ガルバリウム鋼板t0.4 立はげ葺(立平葺)	テラス・ポーチ床	コンクリートコテ仕上げ		
	アスファルトルーフィング(22kg/巻)+合板t12下地	軒天井	珪酸カルシウム板t6 EP		
	断熱材:グラスウールt100(10kg/㎡)	外部幅木	コンクリート打放し		
外壁 1	コンクリート打放し フッ素樹脂クリアー 耐火	軒樋	ガルバリウム鋼板t0.4		
外壁 2	耐水PBt12.5下地 ガルバリウム鋼板スパンドレル張	縦樋	ステンレスパイプ80φ		
告示1359号 第1-11(2)	断熱材:グラスウールt75(10kg/㎡)	水切り類	アルミ		
外壁 3	セメント系サイディングボードt12下地 ジョリバット吹付 PCO30BE-9201	外部開口部	アルミサッシ		
	断熱材:グラスウールt75(10kg/㎡)				

内部仕上表

階	室 名	天井高	床		幅 木	壁		天 井		備 考
		床 高	下 地	仕 上		下 地	仕 上	下 地	仕 上	
1	玄関	CH=2530	モルタル	磁器質100角タイル	化粧MDF H=60	PBt12.5	ビニルクロス	PBt9.5	ビニルクロス	玄関収納
		FL-100								
	廊下	CH=2430	合板t12	MDFフローリングボードt6	↑	↑	↑	↑	↑	
		FL±0	断熱材:発泡ポリスチレンフォームt25							
	リビングダイニング	CH=2430	↑	↑	↑	↑	↑	↑	↑	カーテンレール
		FL±0								
	キッチン	CH=2430	↑	↑	↑	耐水PBt12.5	ビニルクロス(QM-9416)	PBt9.5	ビニルクロス(QM-9416)	流し台:L=2250 レンジフード:L=600 吊戸棚:H=500,W=900+750
		FL±0					一部化粧ケイカル板t6			棚:木製OP
	洗面脱衣	CH=2230	合板t12	クッションフロアt2.0	軟質ビニル幅木 H=60	耐水PBt12.5	ビニルクロス	PBt9.5	ビニルクロス	洗面化粧台:L=600 洗濯機パン:W=750 タオル掛:L=500
		FL±0	断熱材:発泡ポリスチレンフォームt25							棚:塩ビシート貼
	WC	CH=2230	↑	↑	↑	↑	↑	↑	↑	ペーパーホルダー タオル掛 棚:木製OP
		FL±0								
2	廊下	CH=2150	合板t12	MDFフローリングボードt6	化粧MDF H=60	PBt12.5	ビニルクロス	↑	↑	
		FL±0								
	洋室 1	CH=3300	↑	↑	↑	↑	↑	↑	↑	カーテンレール
		FL±0								
	洋室 2	CH=2310	↑	↑	↑	↑	↑	↑	↑	カーテンレール
		FL±0								
	ウォークインクローゼット	CH=2150	↑	↑	↑	↑	↑	↑	↑	ハンガーパイプ 東側室のみカーテンレール
		FL±0								
R	ロフト	CH=1400	↑	↑	↑	↑	↑	↑	↑	
		FL±0								
共通	階段			化粧LVL	化粧LVL	↑	↑	↑	↑	木製手すり
	収納		合板t12	MDFフローリングボードt6	雑巾摺り	PBt9.5	ビニルクロス	↑	↑	クローゼットにはハンガーパイプ

不燃・準不燃リスト

PBt12.5	NM-8619
PBt9.5	QM-9828
耐水PBt12.5	NM-9639
化粧ケイカル板	NM-8579

1

2

3

4

</